


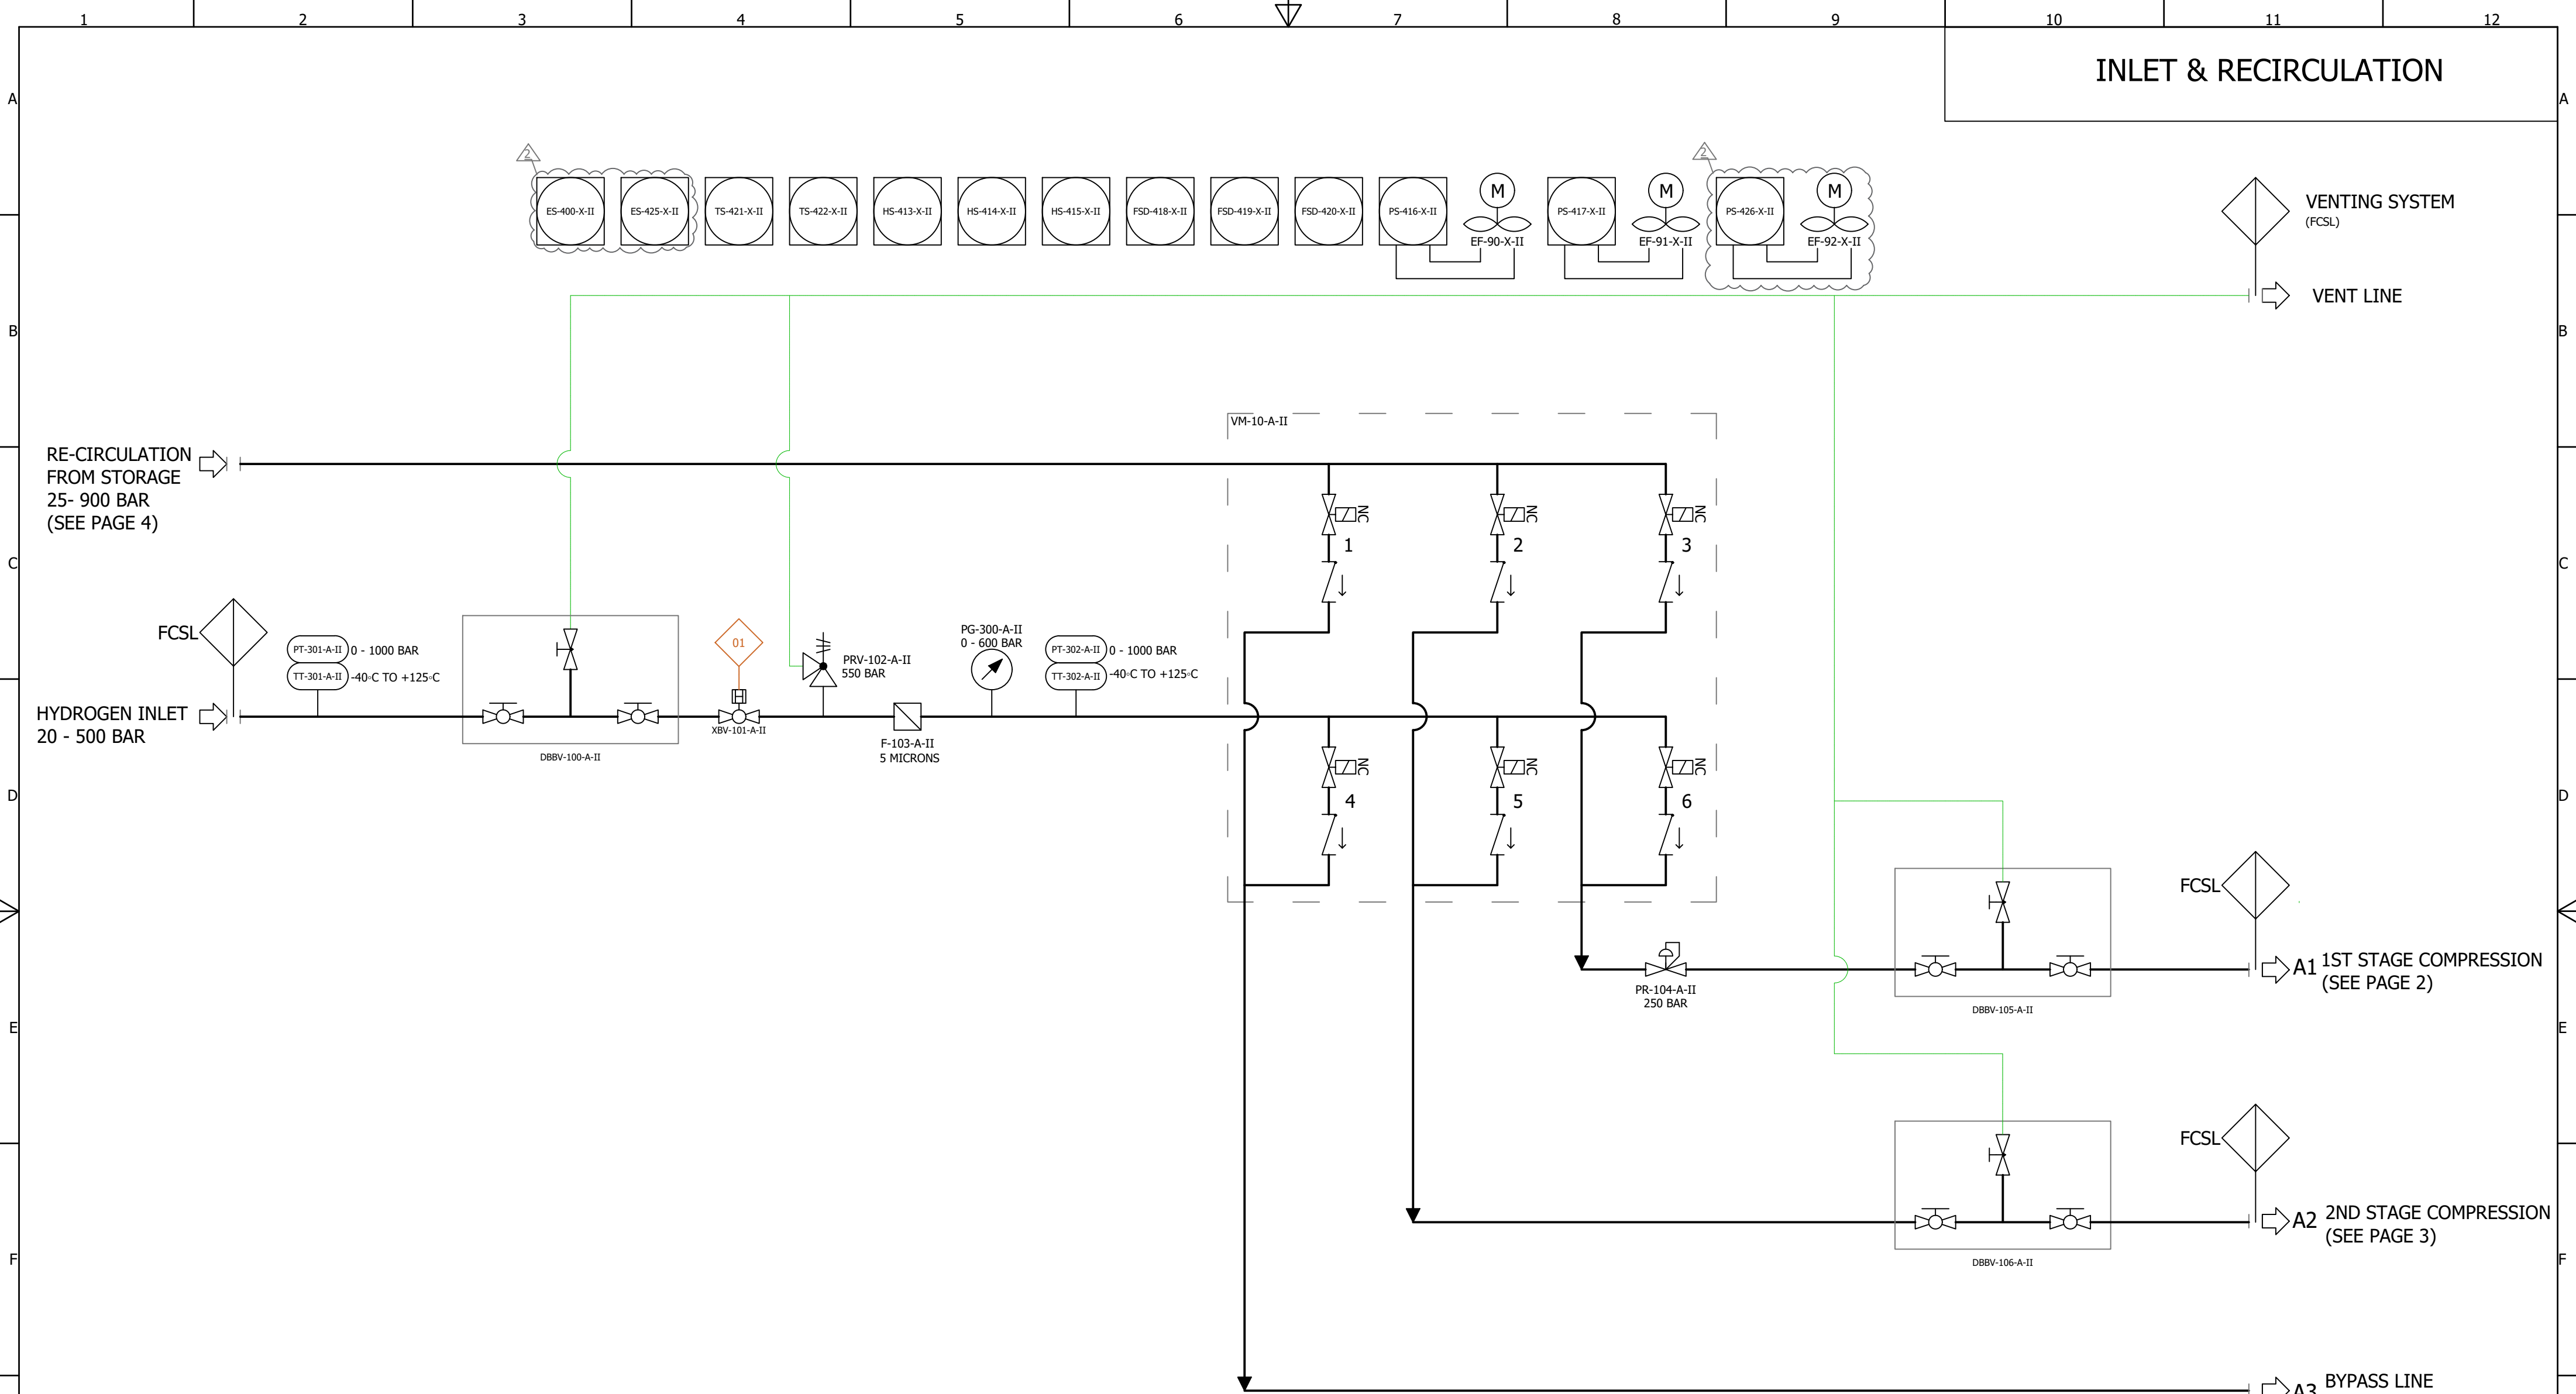

KEY:

9/16" CONE & THREAD

VENT LINE

NOTES:

1. COOLANT FLOW RATE WILL VARY DEPENDING ON CHILLER CHOSEN.

2. COOLANT MANIFOLD TO BE INSULATED.

3. REFER TO DOC NO.SCH-1711-001 FOR EQUIPMENT, INSTRUMENT & VALVE SCHEDULE.

4. TAGS THAT ARE SHOWN IN (BRACKETS) ARE THE ORIGINAL MANUFACTURER TAGS. THEY ARE FOR REFERENCE ONLY.

5. SITE INLET AIR CONNECTION TO BE 1/2" BSPP.

6. VALVE TERMINAL INLET TO BE 10MM.

7. VALVE TERMINAL DISTRIBUTION TO BE 6MM.

EXAMPLE TAG

TAG NAME	PT	0 - 1000 BAR PT - XX
PRESSURE RANGE	0-1000 BAR	
SYMBOL	PT - XX	

BALL VALVE	PRESSURE RELIEF VALVE	THERMAL PRESSURE RELIEF DEVICE	PRESSURE REDUCING REGULATOR	TEMP TRANSMITTER	FILTER	PRESSURE GAUGE	FLEXIBLE HOSE	AIR COMPRESSOR	MOTOR										
NEEDLE VALVE	SOLANOTID VALVE	MODULATING BALL VALVE	BACK PRESSURE REGULATOR	FLOW TRANSMITTER	FLOW METER	TEMP GAUGE	BREAKAWAY COUPLING	OIL/WATER SEPARATOR	PUMP										
CHECK VALVE	PNEUMATICALLY ACTUATED BALL VALVE	MODULATING NEEDLE VALVE	MODULATING PRESSURE REDUCING REGULATOR	PROXIMITY SENSOR	HEAT EXCHANGER	HYDROGEN SENSOR	HYDROGEN NOZZLE	PNEUMATIC SUPPRESSOR	INSULATION	-	2	ECM - 026							
DOUBLE BLOCK & BLEED VALVE	ACTUATED BALL VALVE	ORIFICE PLATE	MODULATING BACK PRESSURE REGULATOR	PRESSURE TRANSMITTER	HVE DISP HZ GAS BOOSTER	TEMPERATURE SENSOR	REFUELING NOZZLE ASSEMBLY	BATTERY LIMITS	E-STOP	-	1	FIRST ISSUE	24/09/2025						
				PT - XX						ZONE	REV	DESCRIPTION	DATE						

REVISION TABLE

Fuel Cell[®] SYSTEMS

STATION YARD,
HUNGERFORD, RG17 0DY
TEL: 01488 507050

EXCLUSIVE PROPERTY OF FUEL CELL SYSTEMS LTD.
ALL RIGHTS RESERVED. NO UNAUTHORIZED COPYING,
MODIFICATION, REPRODUCTION OR DISTRIBUTION.

PROJECT/PRODUCT No.
HFL-30-900

PROJECT/PRODUCT TITLE
HYFLEET 900 BAR 30KG/HR

DRAWN
S.NAEEM

DATE
12/08/2025

APPROVED
G.SHENDGE

DATE
25/09/2025

ALL DIMENSIONS IN METRES
UNLESS STATED OTHERWISE

TITLE
HYFLEET HFL-30-900 P&ID


DRAWING No.
PD-000014

STATUS
WIP


REV
02


SHEET
1 OF 7


1ST STAGE COMPRESSION

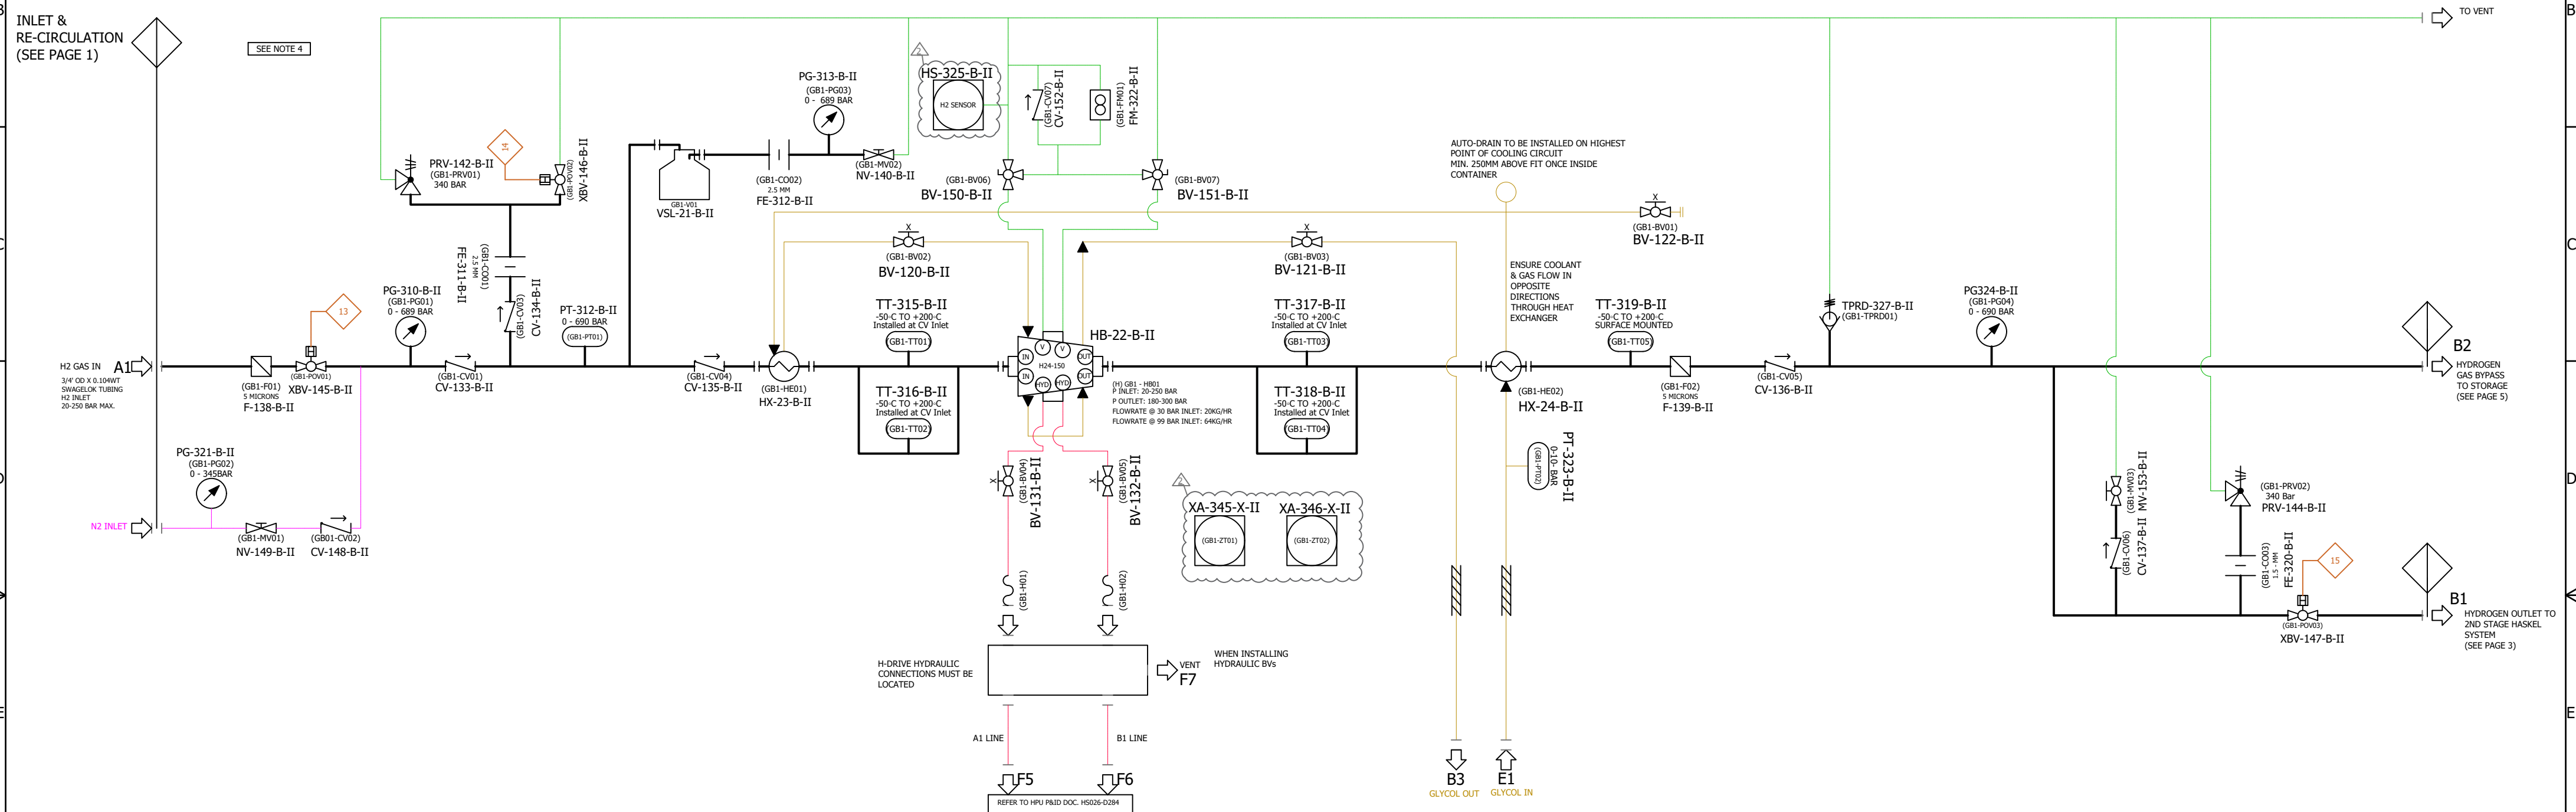


THIS DRAWING IS A HEAVILY SIMPLIFIED SCHEMATIC, REFERENCING THE EQUIPMENT THAT FCSL ARE INTERFACING WITH DIRECTLY. FOR A FULLY DETAILED P&ID, SEE DOCUMENT HSM-1-3-HAA-XX-EU-Q1-10 P&ID FROM THE MANUFACTURER (HASKEL)

 KEY: — 3/4"ODx0.104WT SWAGELOK — VENT LINE — PURGE LINE — HYDRAULIC LINE — COOLANT LINE	EXAMPLE TAG		
	TAG NAME	PT	0 - 1000 BAR 
	PRESSURE RANGE	0-1000 BAR	
	SYMBOL		

 
																		 Fuel Cell[®] SYSTEMS STATION YARD, HUNGERFORD, RG17 0DY TEL: 01488 507050 EXCLUSIVE PROPERTY OF FUEL CELL SYSTEMS LTD. ALL RIGHTS RESERVED. NO UNAUTHORIZED COPYING, MODIFICATION, REPRODUCTION OR DISTRIBUTION.	PROJECT/PRODUCT No. HFL-30-900		TITLE HYFLEET HFL-30-900 P&ID					
																	DRAWN S.NAEEM		DATE 12/08/2025	DRAWING No. PD-000014						
										-	2	ECM - 026					STATUS WIP		REV 01							
										ZONE	REV	DESCRIPTION			DATE		SIZE A2		SHEET 2 OF 7							
																	REVISION TABLE									

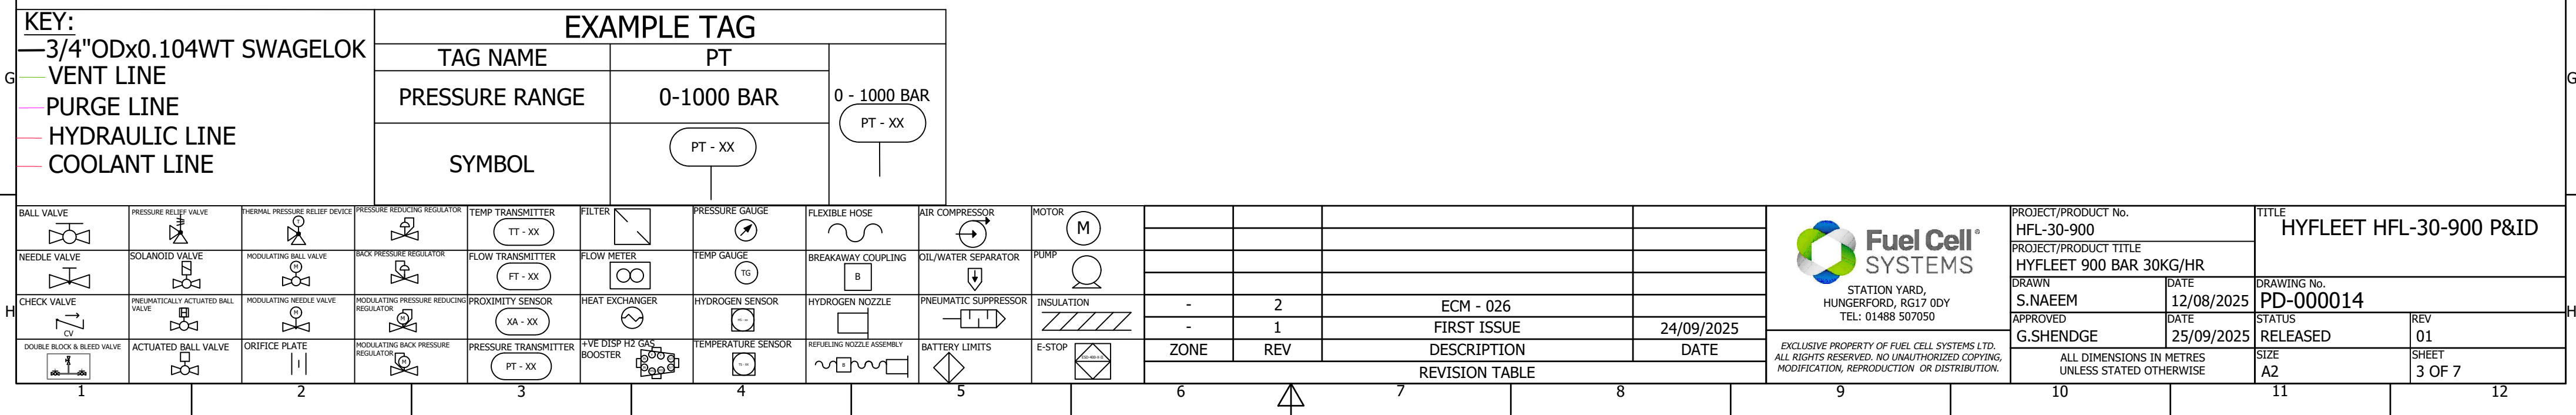

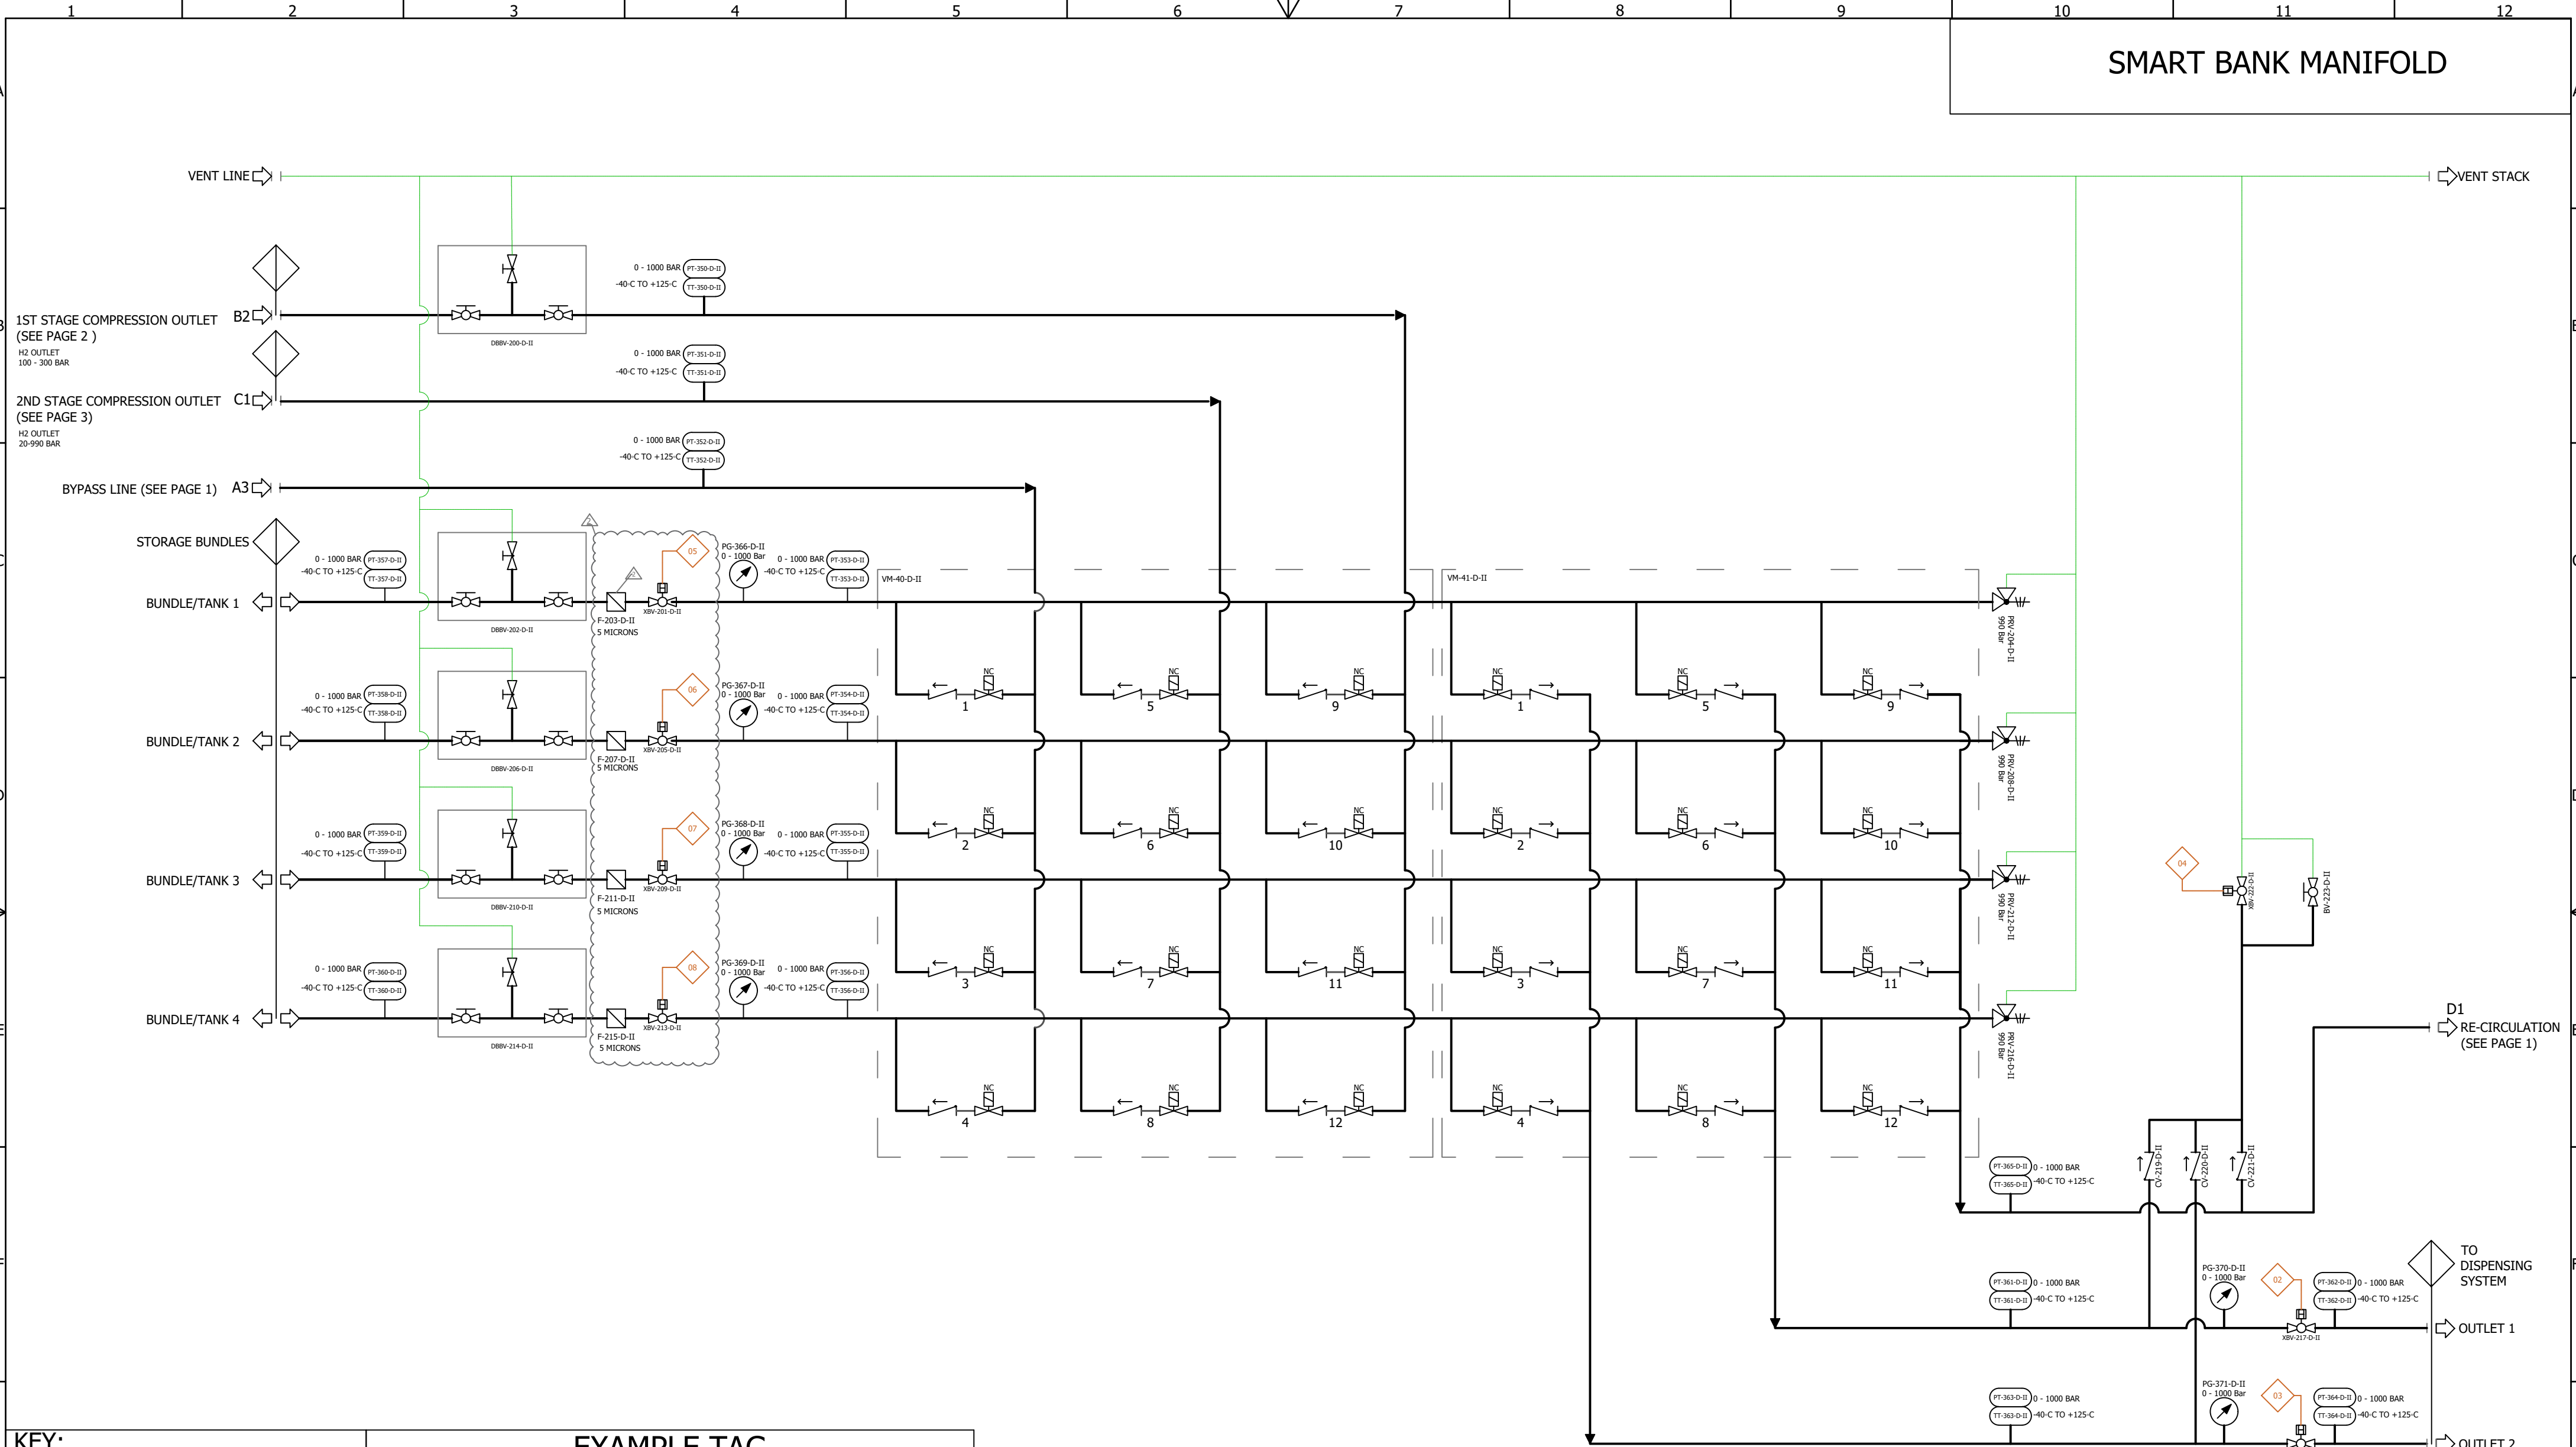

KEY: 9/16" CONE & THREAD VENT LINE	EXAMPLE TAG		
	TAG NAME	PT	0 - 1000 BAR PT - XX
	PRESSURE RANGE	0-1000 BAR	
	SYMBOL	PT - XX	


BALL VALVE	PRESSURE RELIEF VALVE	THERMAL PRESSURE RELIEF DEVICE	PRESSURE REDUCING REGULATOR	TEMP TRANSMITTER TT - XX	FILTER	PRESSURE GAUGE	FLEXIBLE HOSE	AIR COMPRESSOR	MOTOR M				
NEEDLE VALVE	SOLANOID VALVE	MODULATING BALL VALVE	BACK PRESSURE REGULATOR	FLOW TRANSMITTER FT - XX	FLOW METER	TEMP GAUGE TG	BREAKAWAY COUPLING B	OIL/WATER SEPARATOR	PUMP				
CHECK VALVE CV	PNEUMATICALLY ACTUATED BALL VALVE	MODULATING NEEDLE VALVE	MODULATING PRESSURE REDUCING REGULATOR	PROXIMITY SENSOR XA - XX	HEAT EXCHANGER	HYDROGEN SENSOR	HYDROGEN NOZZLE	PNEUMATIC SUPPRESSOR	INSULATION	-	2	ECM - 026	
DOUBLE BLOCK & BLEED VALVE	ACTUATED BALL VALVE	ORIFICE PLATE	MODULATING BACK PRESSURE REGULATOR	PRESSURE TRANSMITTER PT - XX	HVE DISP H2 GAS BOOSTER	TEMPERATURE SENSOR	REFUELING NOZZLE ASSEMBLY	BATTERY LIMITS	E-STOP	-	1	FIRST ISSUE	24/09/2025
										ZONE	REV	DESCRIPTION	DATE
REVISION TABLE													

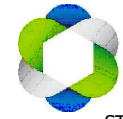**Fuel Cell
SYSTEMS**

STATION YARD,
HUNGERFORD, RG17 0DY
TEL: 01488 507050

EXCLUSIVE PROPERTY OF FUEL CELL SYSTEMS LTD.
ALL RIGHTS RESERVED. NO UNAUTHORIZED COPYING,
MODIFICATION, REPRODUCTION OR DISTRIBUTION.

PROJECT/PRODUCT No. HFL-30-900		TITLE HYFLEET HFL-30-900 P&ID	
PROJECT/PRODUCT TITLE HYFLEET 900 BAR 30KG/HR		DRAWING No. PD-000014	
DRAWN S.NAEEM	DATE 12/08/2025	STATUS WIP	
APPROVED G.SHENDGE	DATE 25/09/2025	SIZE A2	REV 01
ALL DIMENSIONS IN METRES UNLESS STATED OTHERWISE		SHEET 4 OF 7	

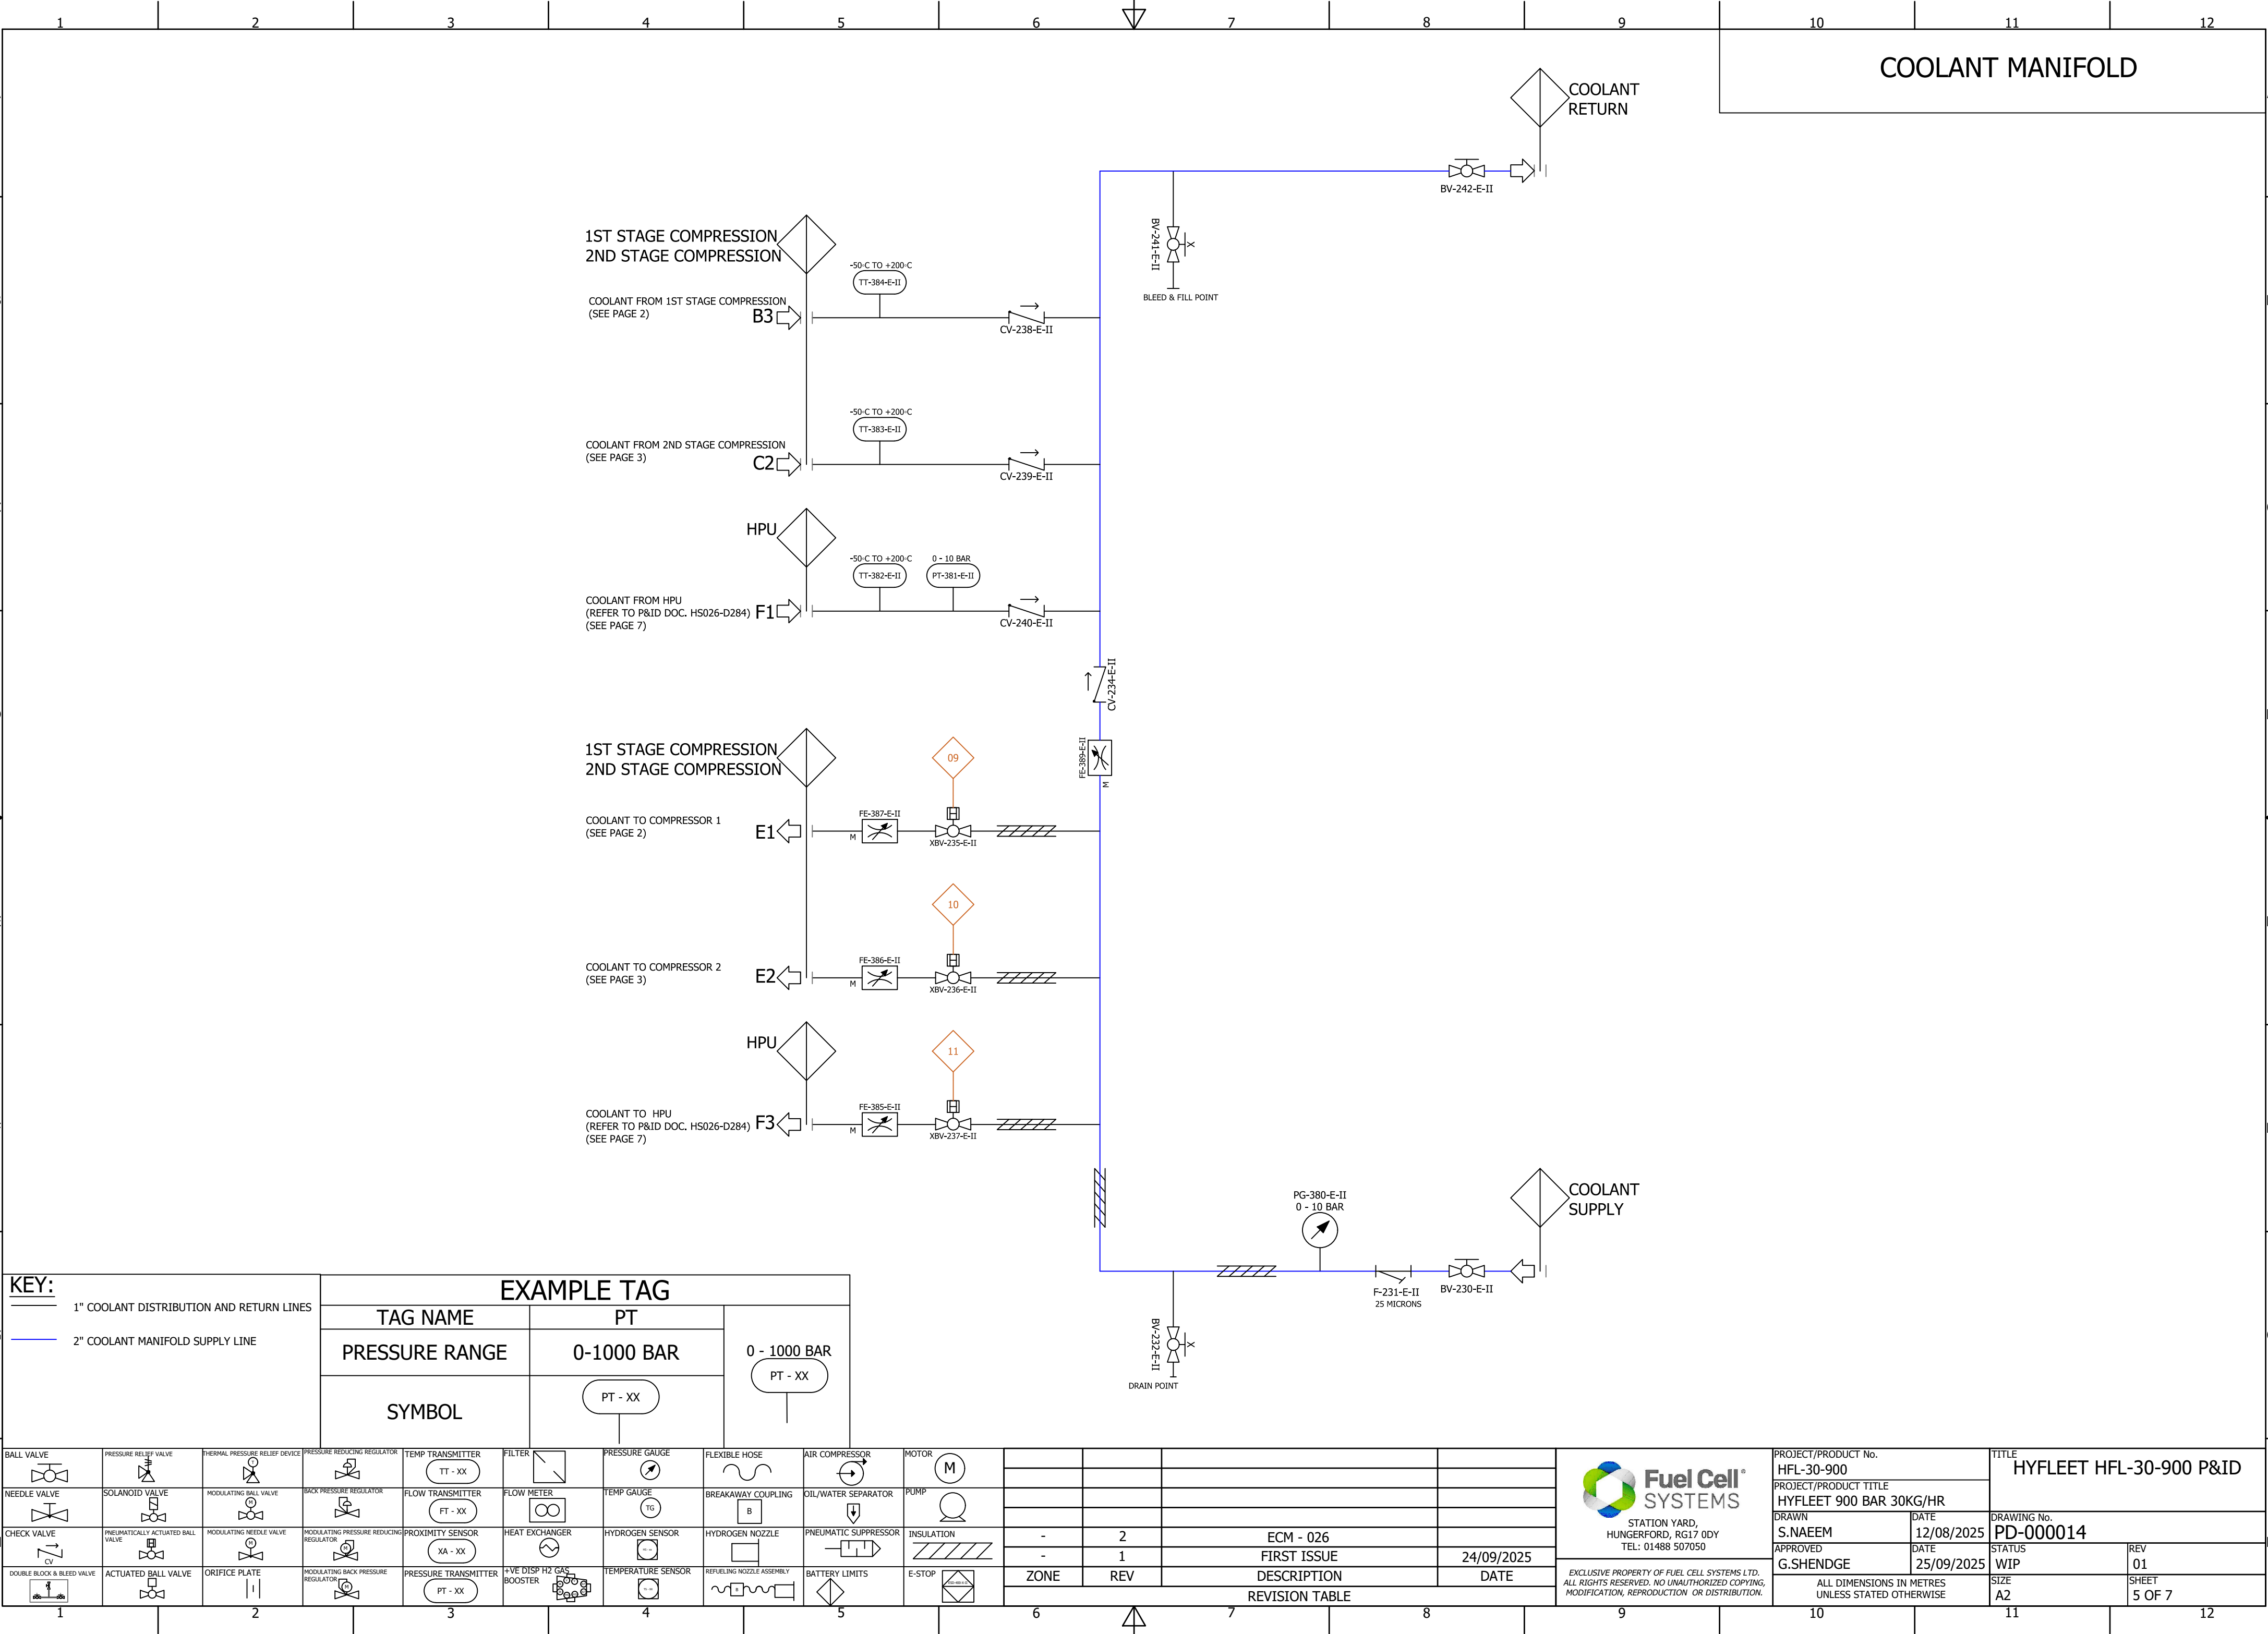

KEY:

1" COOLANT DISTRIBUTION AND RETURN LINES

2" COOLANT MANIFOLD SUPPLY LINE

EXAMPLE TAG		
TAG NAME	PT	0 - 1000 BAR PT - XX
PRESSURE RANGE	0-1000 BAR	
SYMBOL	PT - XX	

BALL VALVE	PRESSURE RELIEF VALVE	THERMAL PRESSURE RELIEF DEVICE	PRESSURE REDUCING REGULATOR	TEMP TRANSMITTER	FILTER	PRESSURE GAUGE	FLEXIBLE HOSE	AIR COMPRESSOR	MOTOR
NEEDLE VALVE	SOLANOID VALVE	MODULATING BALL VALVE	BACK PRESSURE REGULATOR	FLOW TRANSMITTER	FLOW METER	TEMP GAUGE	BREAKAWAY COUPLING	OIL/WATER SEPARATOR	PUMP
CHECK VALVE	PNEUMATICALLY ACTUATED BALL VALVE	MODULATING NEEDLE VALVE	MODULATING PRESSURE REDUCING REGULATOR	PROXIMITY SENSOR	HEAT EXCHANGER	HYDROGEN SENSOR	HYDROGEN NOZZLE	PNEUMATIC SUPPRESSOR	INSULATION
DOUBLE BLOCK & BLEED VALVE	ACTUATED BALL VALVE	ORIFICE PLATE	MODULATING BACK PRESSURE REGULATOR	PRESSURE TRANSMITTER	+VE DISP H2 GAS BOOSTER	TEMPERATURE SENSOR	REFUELING NOZZLE ASSEMBLY	BATTERY LIMITS	E-STOP


ZONE	REV	DESCRIPTION	DATE
-	2	ECM - 026	
-	1	FIRST ISSUE	24/09/2025
ZONE	REV	DESCRIPTION	DATE

PROJECT/PRODUCT No. HFL-30-900		TITLE HYFLEET HFL-30-900 P&ID	
PROJECT/PRODUCT TITLE HYFLEET 900 BAR 30KG/HR		DRAWING No. PD-000014	
DRAWN S.NAEEM	DATE 12/08/2025	STATUS WIP	REV 01
APPROVED G.SHENDGE	DATE 25/09/2025	SIZE A2	SHEET 5 OF 7
ALL DIMENSIONS IN METRES UNLESS STATED OTHERWISE			

Fuel Cell[®] SYSTEMS

STATION YARD,
HUNGERFORD, RG17 0DY
TEL: 01488 507050

EXCLUSIVE PROPERTY OF FUEL CELL SYSTEMS LTD.
ALL RIGHTS RESERVED. NO UNAUTHORIZED COPYING,
MODIFICATION, REPRODUCTION OR DISTRIBUTION.

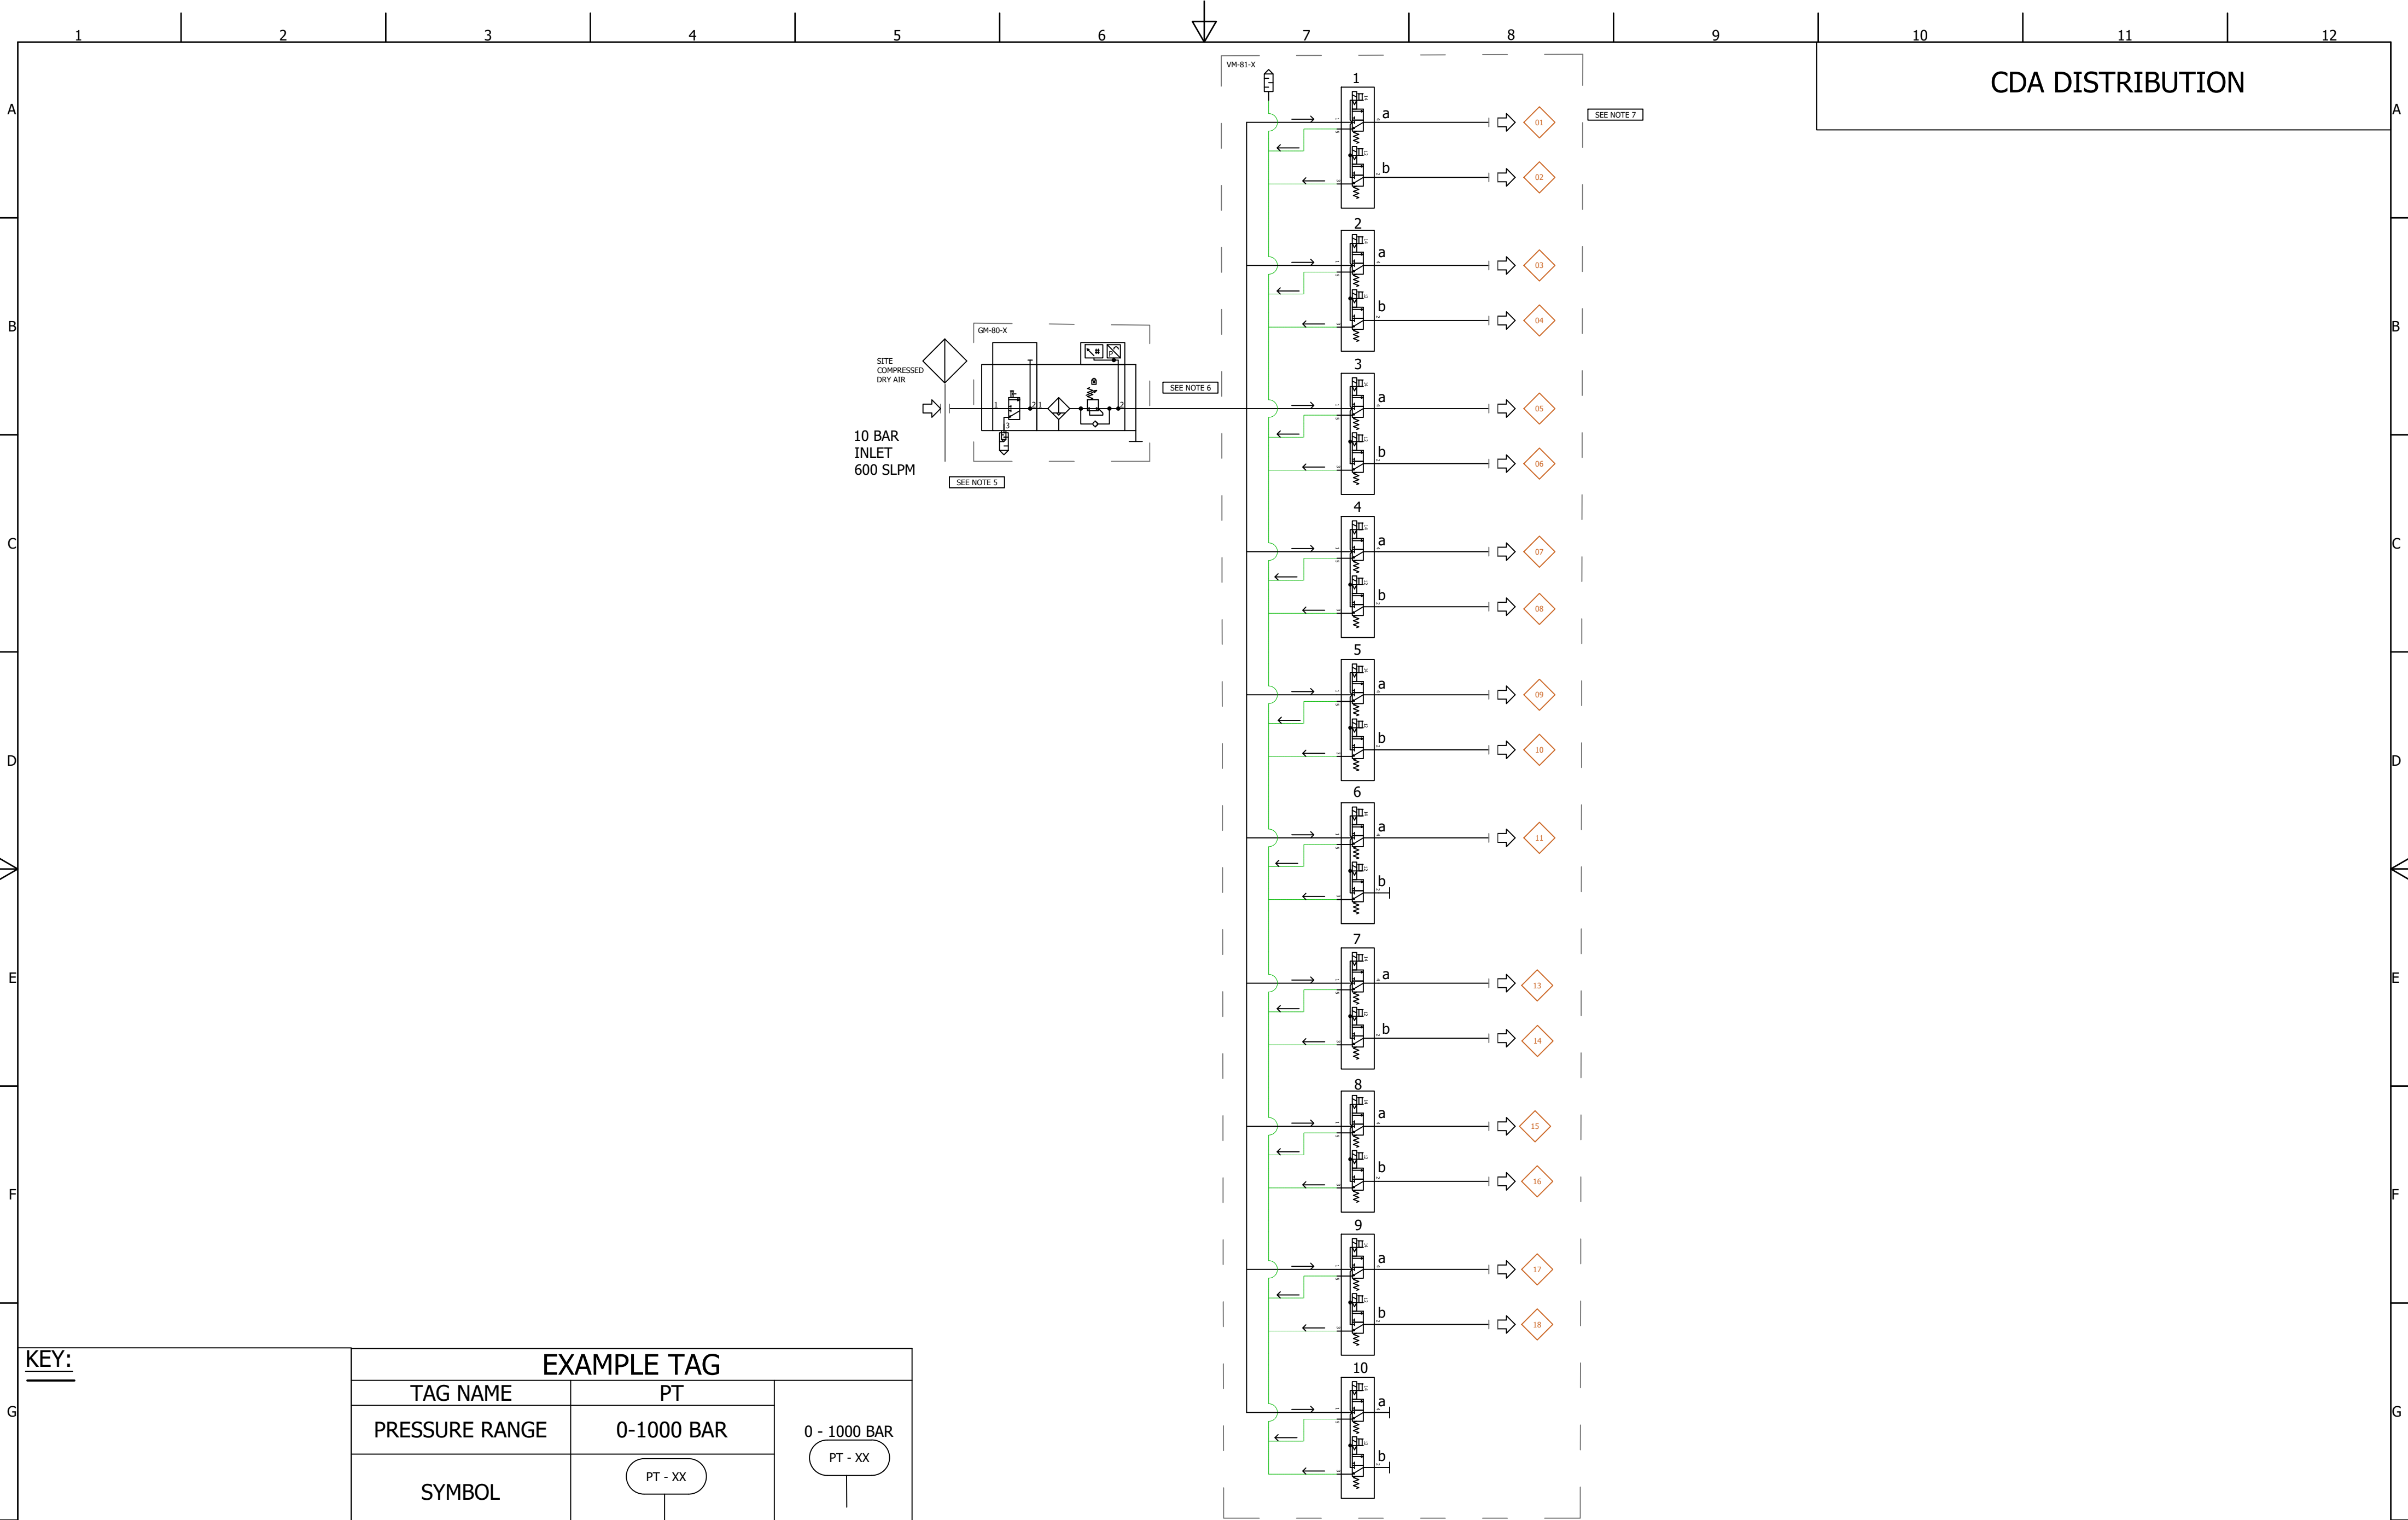[illegible]

